

A PROPRIEDADE INTELECTUAL DESTES DESENHO É TRATADA NO CONTRATO, SENDO QUE A EMPRESA NÃO SE RESPONSABILIZA POR QUALQUER USO NÃO AUTORIZADO. A EMPRESA SE RESPONSABILIZA POR QUALQUER USO NÃO AUTORIZADO. A EMPRESA SE RESPONSABILIZA POR QUALQUER USO NÃO AUTORIZADO.



INSTRUÇÕES P/ PLANTAS	
COR	ESPESURA
COB. N.º 1	0,05
WHITE	0,1
YELLOW	0,1
GREEN	0,2
CYAN	0,3
BLUE	0,4
RED	0,6
MAGENTA	0,8

- NOTAS**
- 1 - TODAS AS DIMENSÕES ESTÃO EM MILÍMETROS, EXCETO ONDE INDICADO.
 - 2 - PARA ISOMÉTRICO VER 2010SA-T-01090.
 - 3 - PARA CADERNO DE SUPORTES, VER 2010SA-T-01089.
 - 4 - PARA LISTA DE MATERIAIS, VER DOC. LM-2001SA-T-01007.
 - 5 - DIMENSÕES COM A INDICAÇÃO *, DEVERÃO SER CONFIRMADAS E AJUSTADAS NA MONTAGEM.


- DOCUMENTOS DE REFERÊNCIA**
- DF-2009-M-603-M-13500 - PILHA DE ESTOCAGEM SECUNDÁRIA - TRANSPORTADOR DE CORREIA - TR-2009-04 (1800) - ARRANJO GERAL.
- 2010SA-M-70253 - BENEFICIAMENTO - PILHA DE ESTOCAGEM SECUNDÁRIA - ADEQUAÇÃO A PNR E MELHORIAS DE USINA (SALOBO 1 E 2) - COBERTURA DE PROTEÇÃO SOB OS TR's NA ÁREA DE TRÂNSITO - TR-2009-04 - CONJUNTO E DETALHES - OPÇÃO 2
- ET-T-410 - ESPECIFICAÇÃO GERAL PARA MATERIAL DE TUBULAÇÃO ENGENHARIA.
- ET-T-408 - ESPECIFICAÇÃO TÉCNICA PARA SUPORTES DE TUBULAÇÕES ENGENHARIA.
- ET-M-412 - ESPECIFICAÇÃO TÉCNICA DE PINTURA PARA PROTEÇÃO ANTICORROSIVA E ACABAMENTO ENGENHARIA.

A		B		EMISSÃO INICIAL		CP		MSJR		GAB		LPS		23/03/26	
REV.		T.E.		DESCRIÇÃO		PROJ.		DES.		VER.		APR.		AUT.	
T.E.		TIPO DE		EMIÇÃO		REVISÕES		(A) PRELIMINAR		(C) PARA CONHECIMENTO		(E) PARA CONSTRUÇÃO		(G) CONFORME CONSTRUÍDO	
(B) PARA APROVAÇÃO		(D) PARA COTAÇÃO		(F) CONFORME COMPRADO		(H) CANCELADO									



				CLASSIFICAÇÃO
PROJETO		Nº DO PROJETO OU SE		USO INTERNO
SISTEMA DE LIMPEZA AUTOMÁTICA DO CHAPEU CHINES		202501996467		
PROJETO DETALHADO		Nº DO CONTRATO		5900121581
BENEFICIAMENTO - PRENSAGEM - HPGR				
SISTEMA DE LIMPEZA AUTOMÁTICA DO CHAPEU CHINES				
TRANSPORTADOR DE CORREIA TR-2010-03 - ÁREA DE TRÂNSITO				
PLANTAS E CORTE				
ESCALA		Nº CONTRATADA		REVISÃO
1: 50		D6-SLB0-0074-T-000002		A
		Nº VALE		
		2010SA-T-01087		

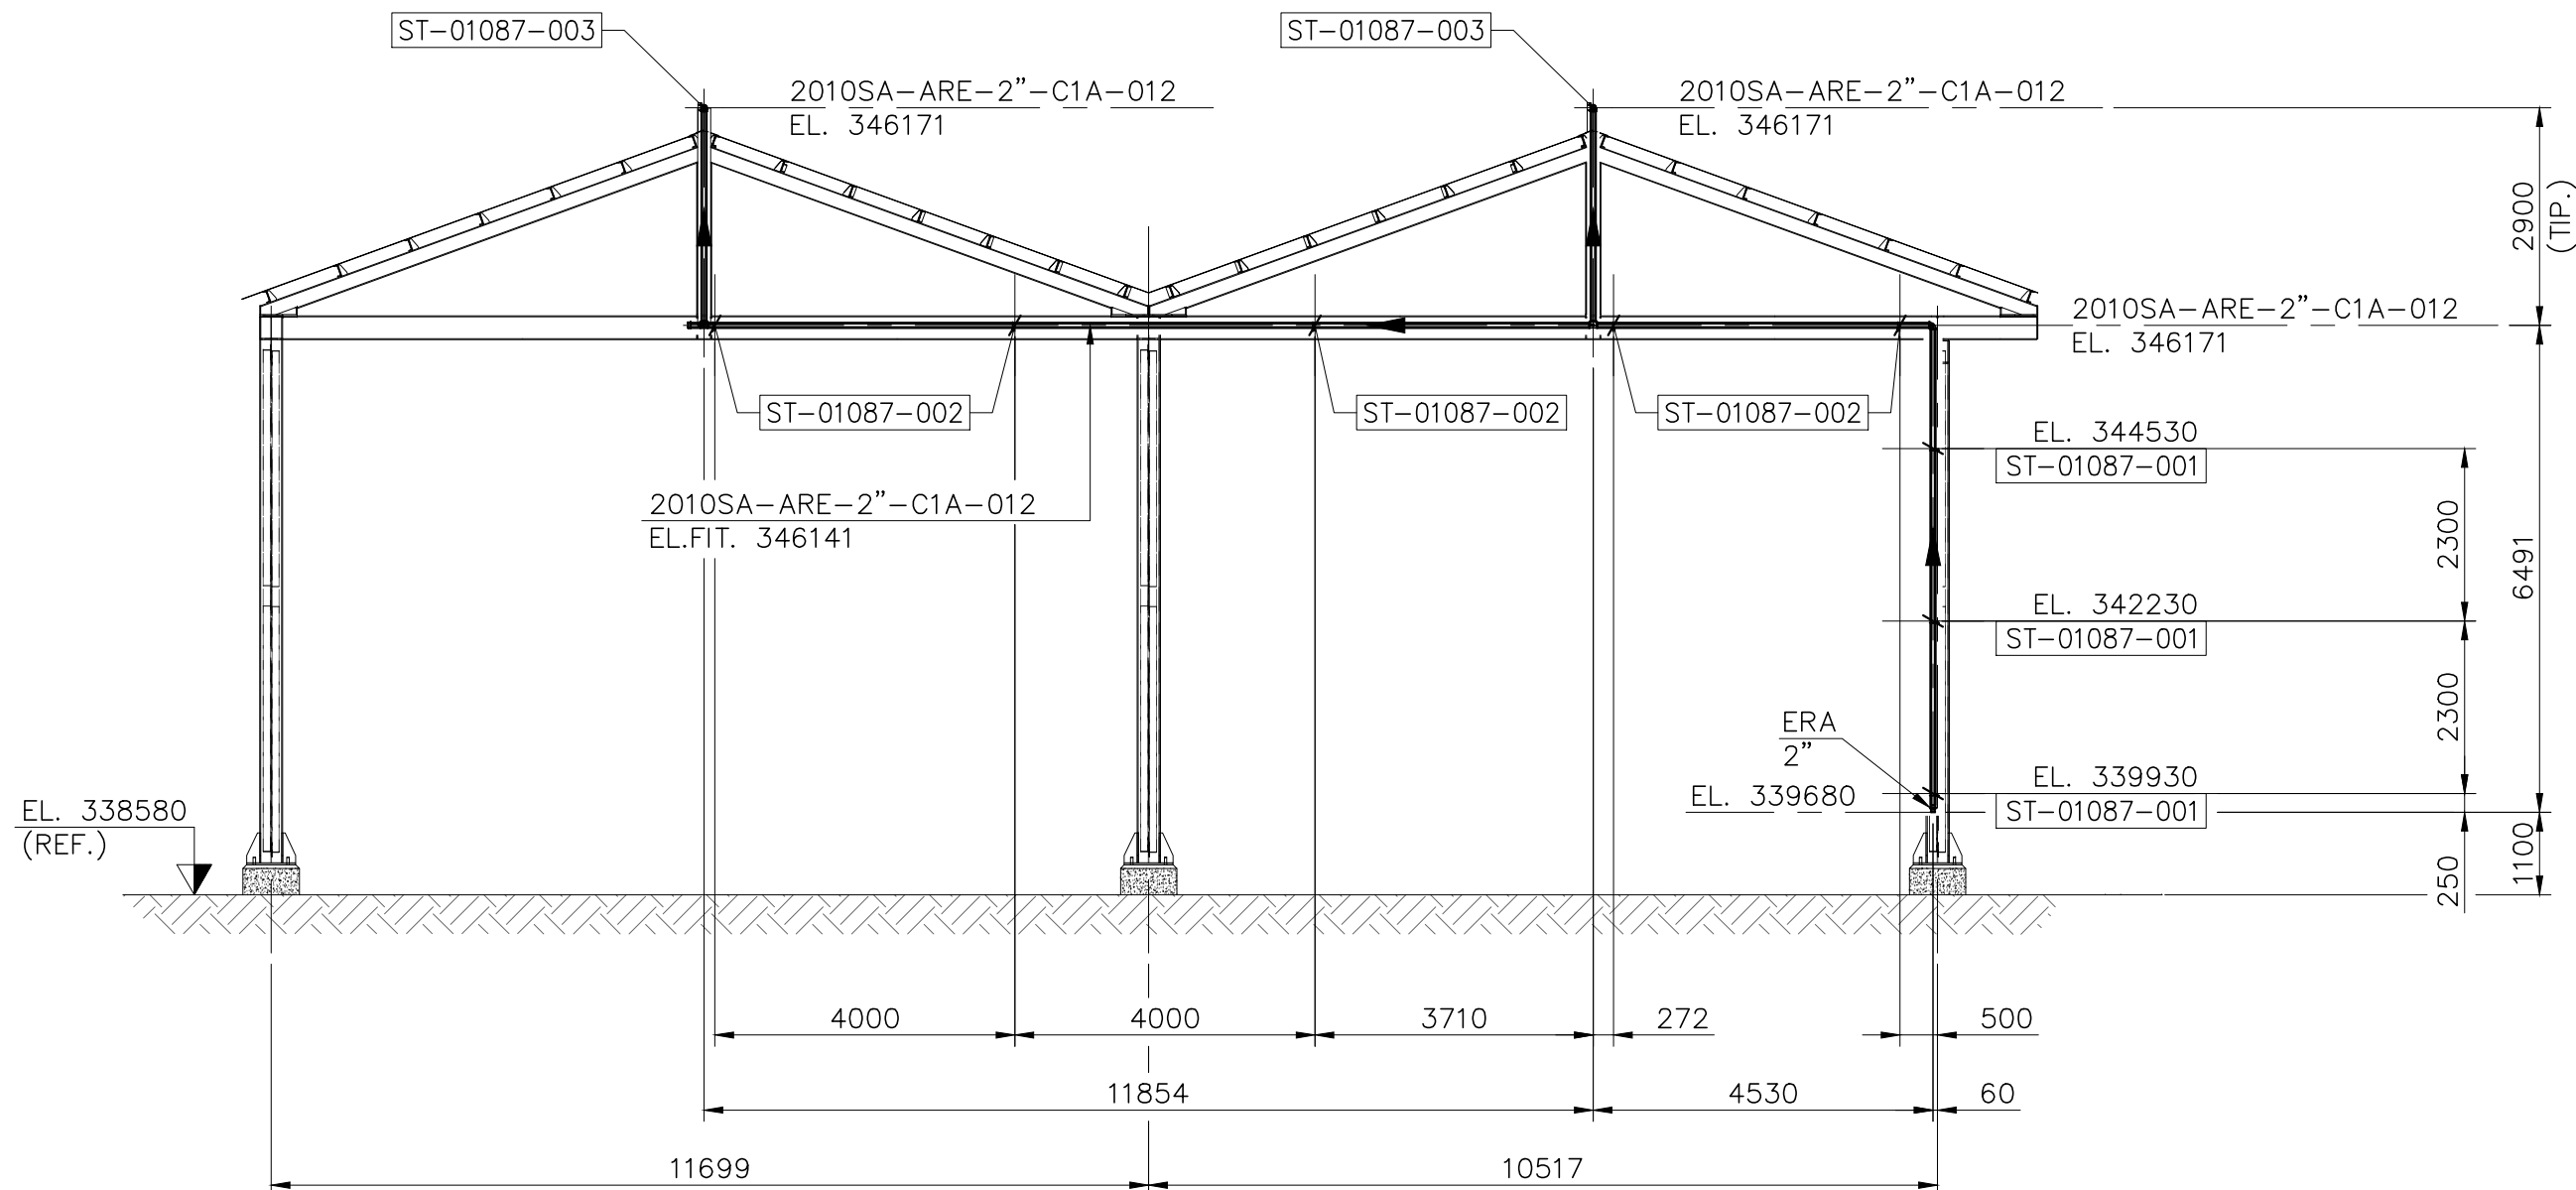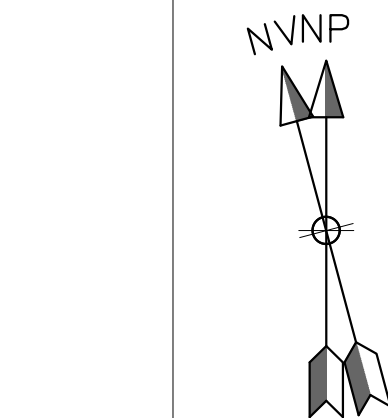


CORTE A-A
ESC. 1:100

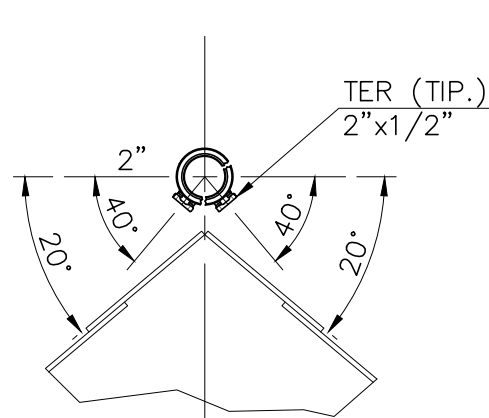

DETALHE BICOS
ESC. 1:10

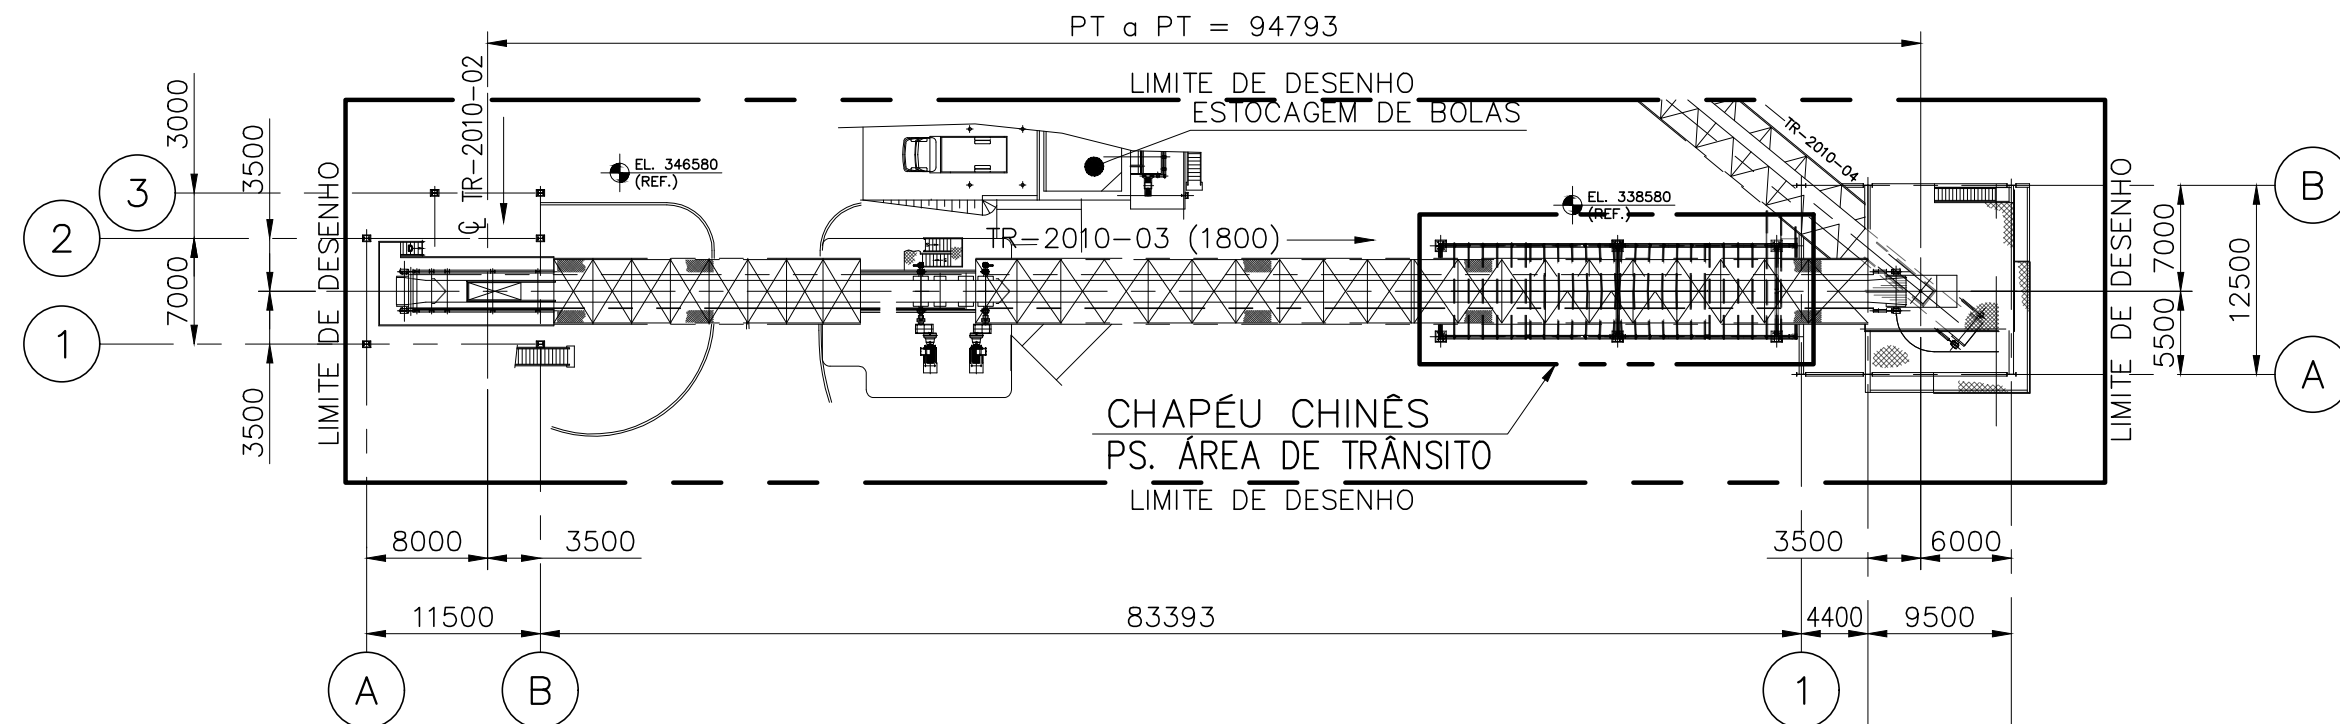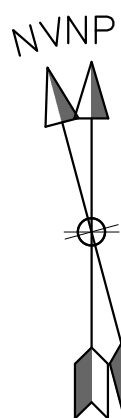

PLANTA DE LOCAÇÃO
ESC. 1:500

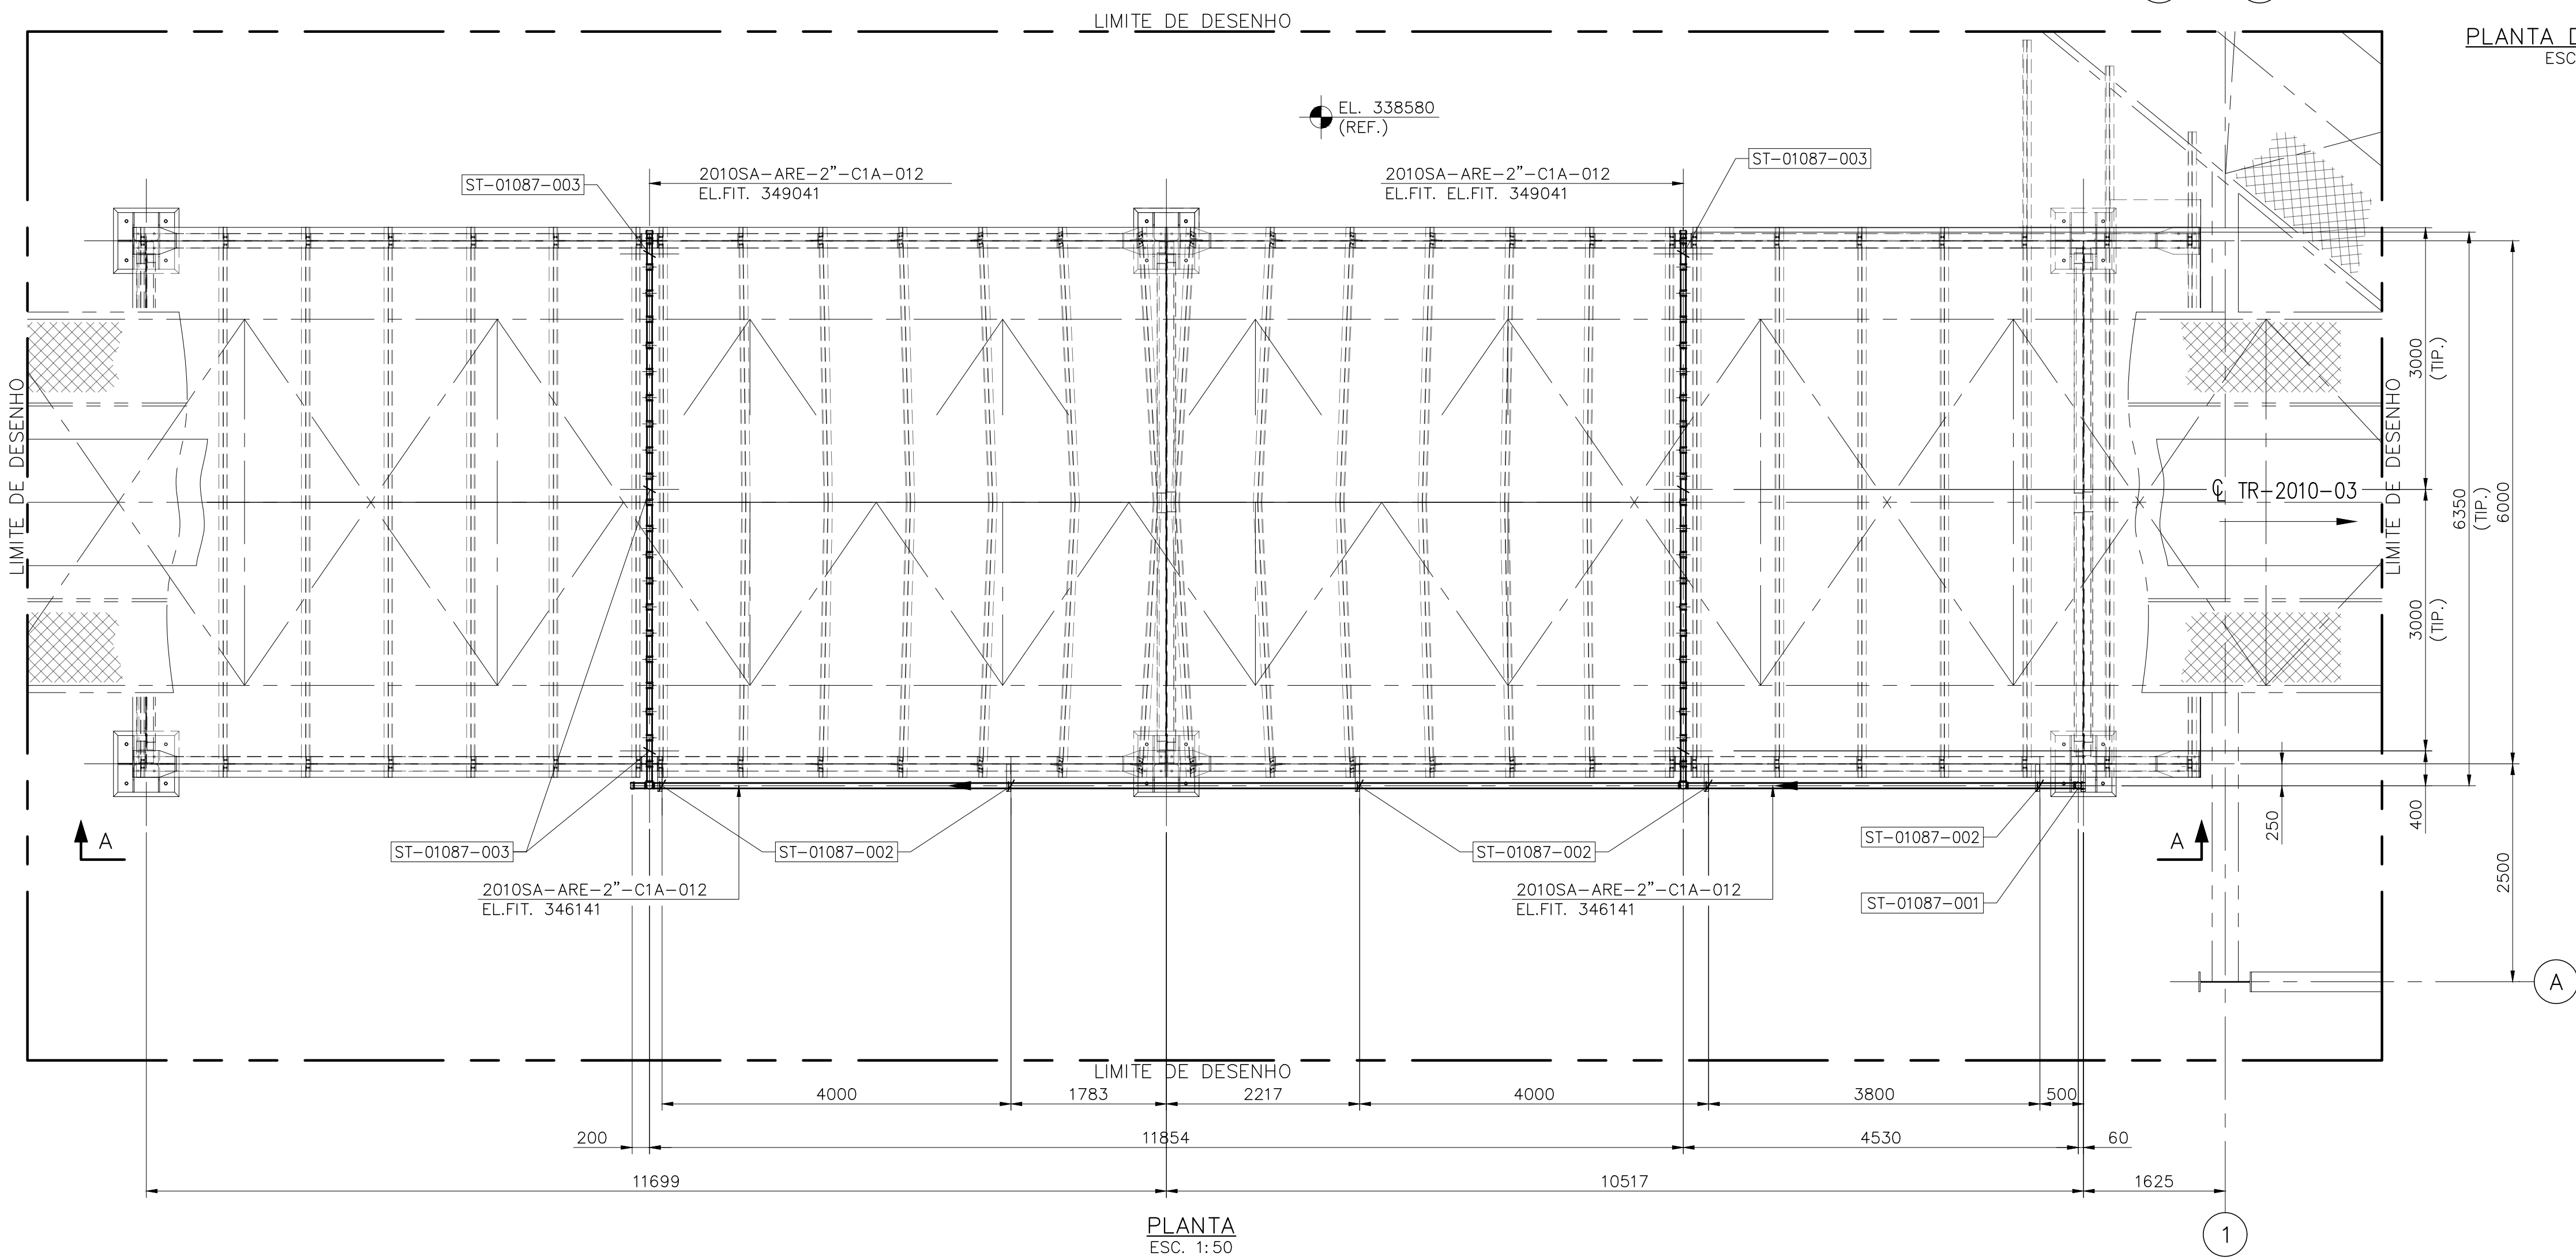

LEGENDA:

- TUBULAÇÃO PROJETADA
- ARE - ÁGUA DE REUSO
- ERA - CONJ. ACOPLADOR TIPO ENGATE RÁPIDO
- TER - TÊ DE REDUÇÃO
- TR - TRANSPORTADOR DE CORREIA
- FIT - FACE INFERIOR DO TUBO
- PS. - PASSAGEM
- ST. APOIO
- ST-XXXX-YYY - N° SEQUENCIAL
- N° PLANTA
- SUPORTE